

DETAIL : - DATE 15/04/26

PLAN FOR MR.DEEPAK KUMAR S/O.KAUSHAL
KISHORE,ADD.-PLOT PART OF GATA
NO.-220,SITUATED AT-RAJSAW
GRAM.-PALTUPUR,PARGANA AND
TEHSIL-GHATAMPUR,AND DISTRICT-KANPUR
NAGAR

AREA STATEMENT AS PER BUILDING BYE
LAWS (2008) REVISED ON 2011,2016 AND
2018

TOTAL PLOT AREA :- 800 SQ.FT.
GROUND FLOOR COVD. AREA :- 600 SQ.FT.
FIRST FLOOR COVD. AREA :- 600 SQ.FT.
SECOND FLOOR COVD. AREA :- 400 SQ.FT.
TOTAL PERMISSIBLE COVD AREA 1600 SQ.FT
PERMISSIBLE GROUND COVERAGE IN :-75%
PERMISSIBLE F.A.R :2.0

AREA STATEMENT AS PER
CLIENT'S/APPLICANT'S CONSENT

TOTAL PLOT AREA :- 800 SQ.FT.
GROUND FLOOR COVD. AREA :- 800 SQ.FT.
FIRST FLOOR COVD. AREA :- 00 SQ.FT.
SECOND FLOOR COVD. AREA :- 00 SQ.FT.
TOTAL COVD. AREA :- 800 SQ.FT.
GRUND COVERAGE IN %:100

BOUNDARY DETAIL :-

EAST- LAND OF ASHOK KUMAR
WEST:- LAND OF SELLER
NORTH:- PLOT OF PRIYANKA SACHAN AND OTHER'S
SOUTH:- 17' WIDE ROAD

SPECIFICATIONS AND GENERAL REMARKS

01. NBC 2016 MUST BE FOLLOWED STRICTLY/AS PER SITE ENGINEER IN
CHARGE.
02. APPROVAL OF THE BUILDING PLAN BY THE LOCAL COMPETENT AUTHORITY
IS COMPULSORY. IN ANY CIRCUMSTANCE BEFORE CONSTRUCTION
03. LAND USE/LAND LEFT COULD BE DETERMINED AFTER VISITING THE SITE
OR AT THE TIME OF SUBMISSION OF MAP ON ONLINE PORTAL OF COMPETENT
AUTHORITY
04. THIS BUILDING PLAN IS NOT PREPARED ON BASIS OF BUILDING CODE ,
BUT ON BASIS OF CLIENT CONSENT

DOOR WINDOW SCHEDULE

S.NO.	TYPE	SIZE	SILL
1.	D	4'-0"X7'-0"	0"
2.	D1	3'-6"X7'-0"	0"
3.	D2	3'-0"X7'-0"	0"
4.	D3	2'-6"X7'-0"	0"
5.	W1	6'-0"X5'-0"	2'-9"
6.	W2	5'-0"X5'-0"	2'-9"
7.	W3	4'-0"X4'-0"	3'-0"
8.	V	2'-6"X2'-0"	5'-0"
9.	D/W	8'-0"X7'-0"	2'-0"


LAND USE DRAWING TITLE DIRECTION

RESIDENTIAL		
-------------	--	--


LEGEND	REMARK
PROP. WORK	
SEWER LINE	
DRAIN LINE	
R.W.P	
TREE	
SOLAR SYSTEM	
OWNER'S SIGN.	NOTE

ARCHITECT/ENGINEER SIGN.


Kalpriksha Design's
Er. Shubham Upadhyay
Regd. AM3121561
Mob: 7068500996

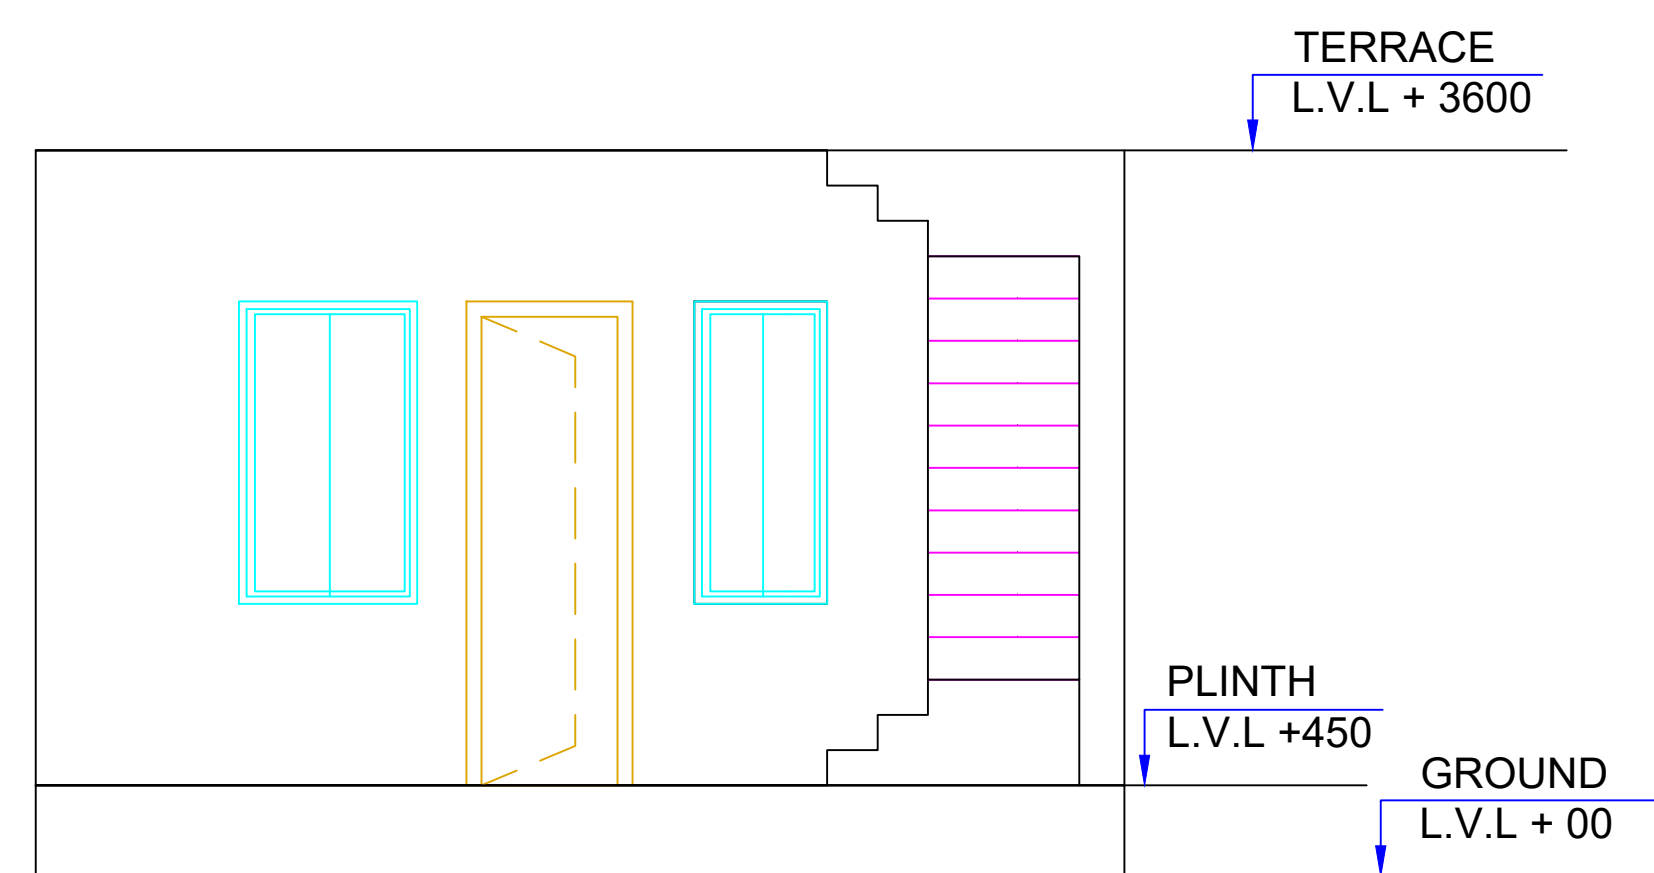


FRONT
ELEVATION

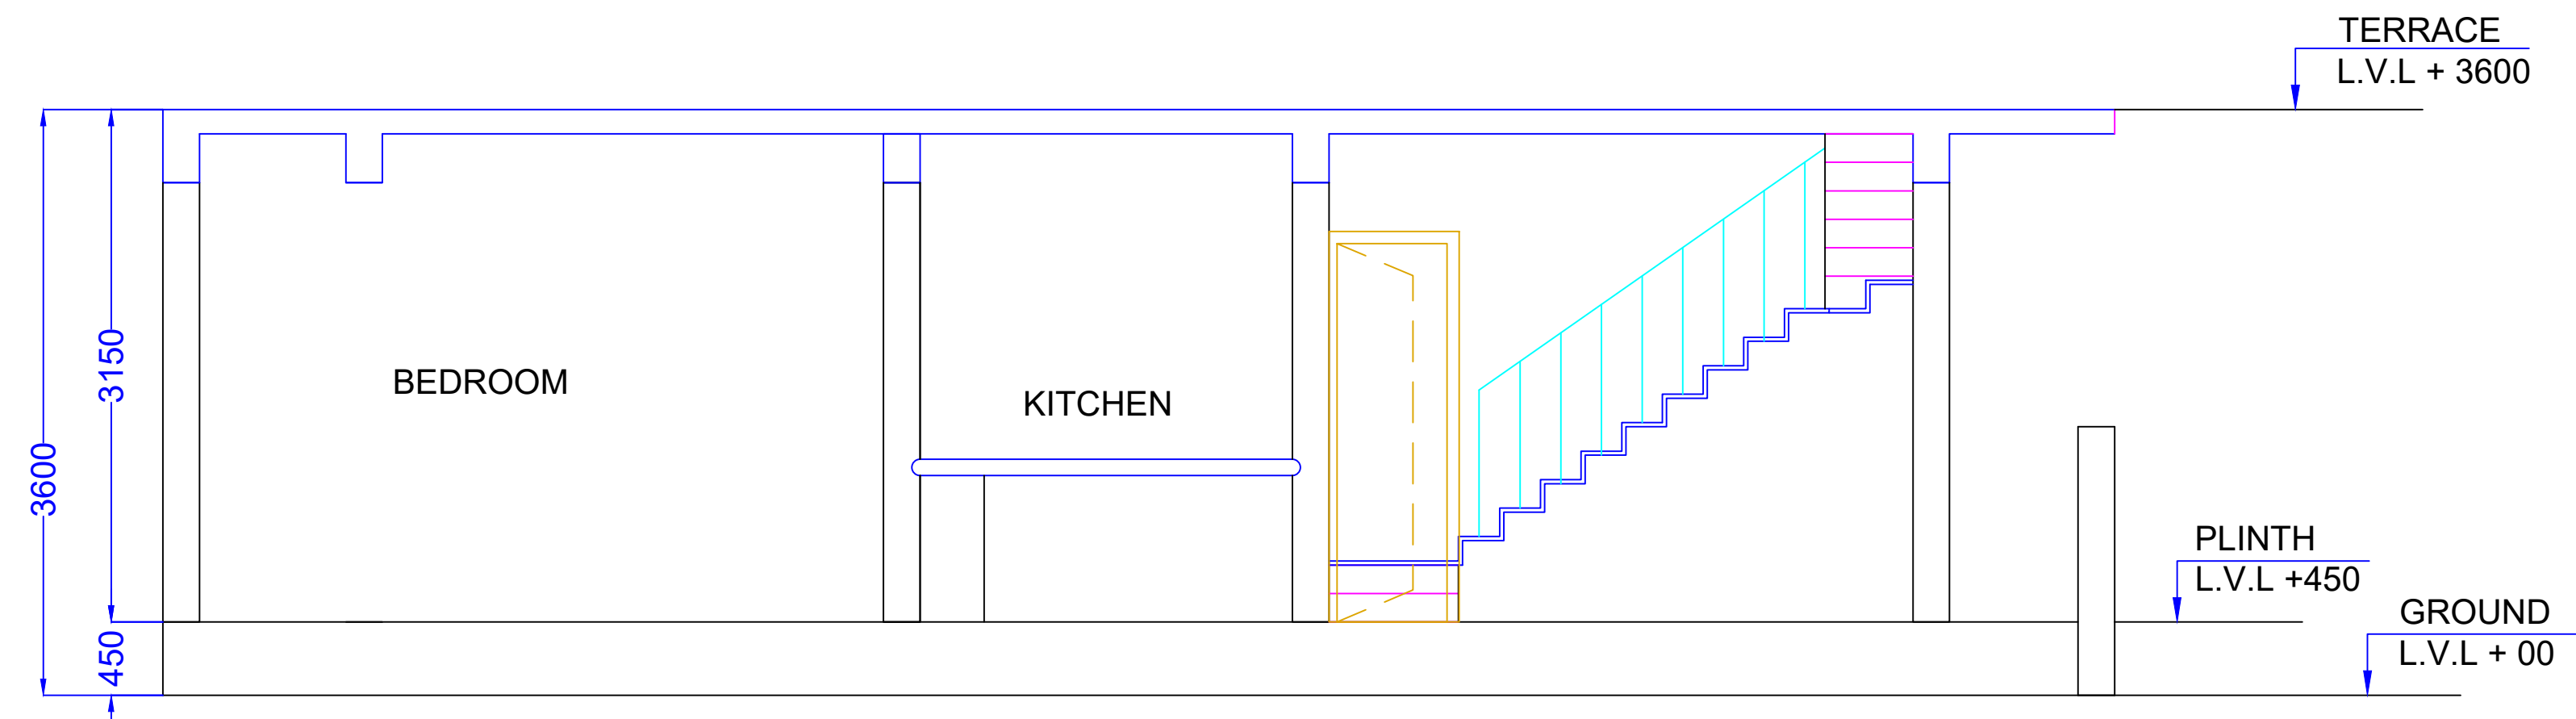


SECTION AT X-X'

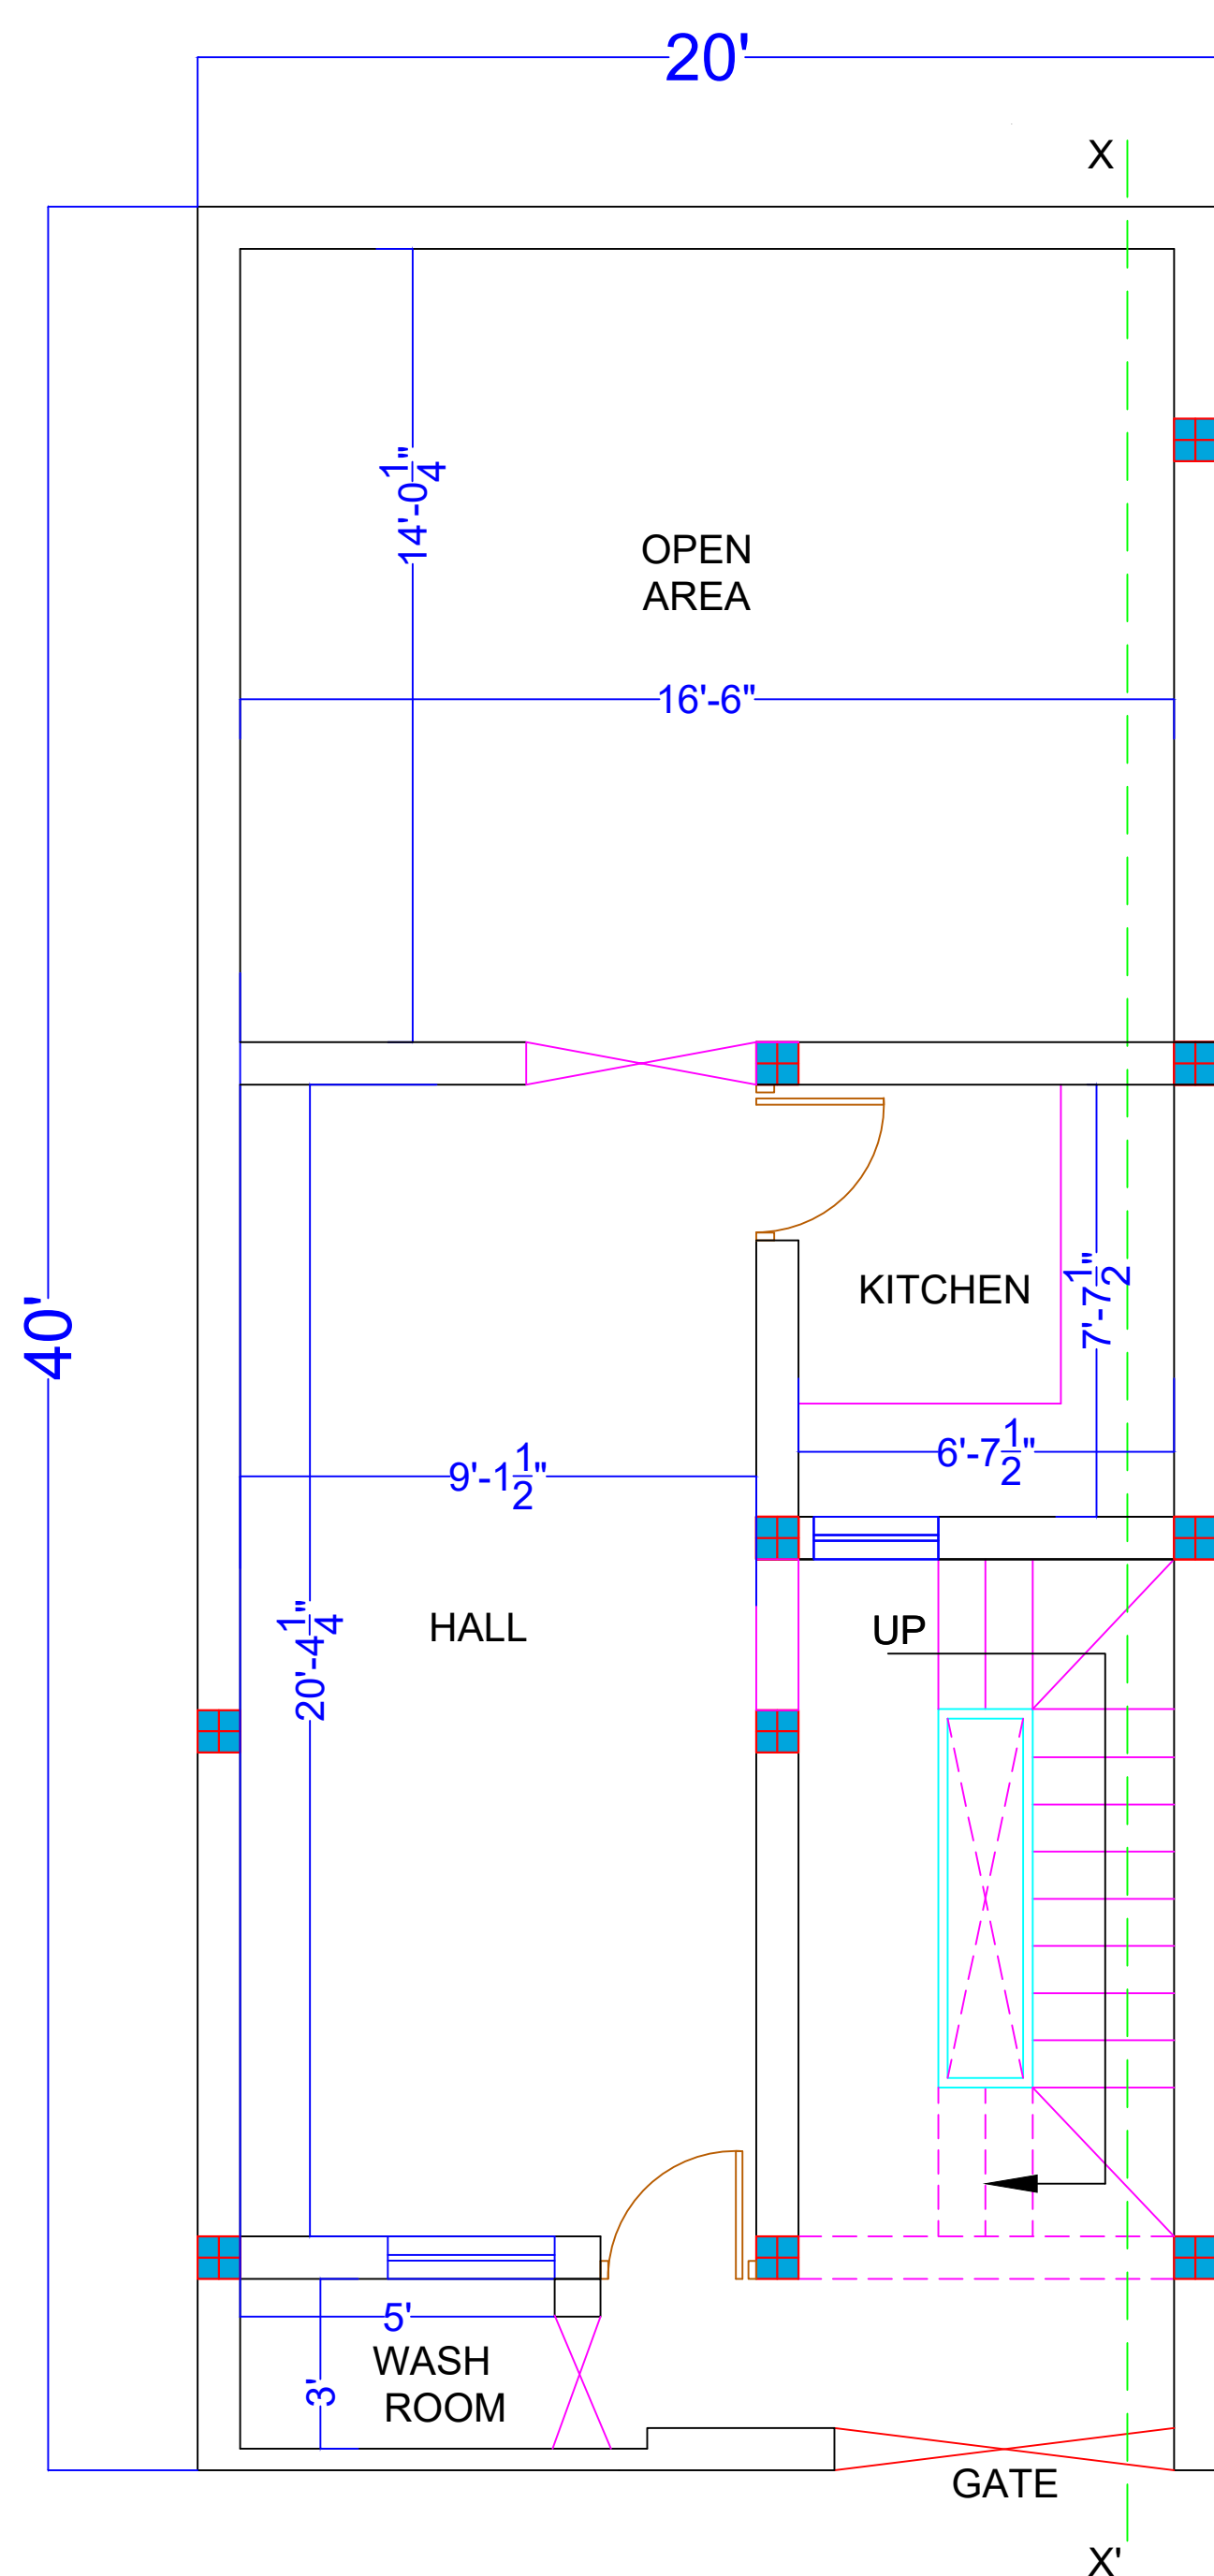

GROUND FLOOR
PLAN

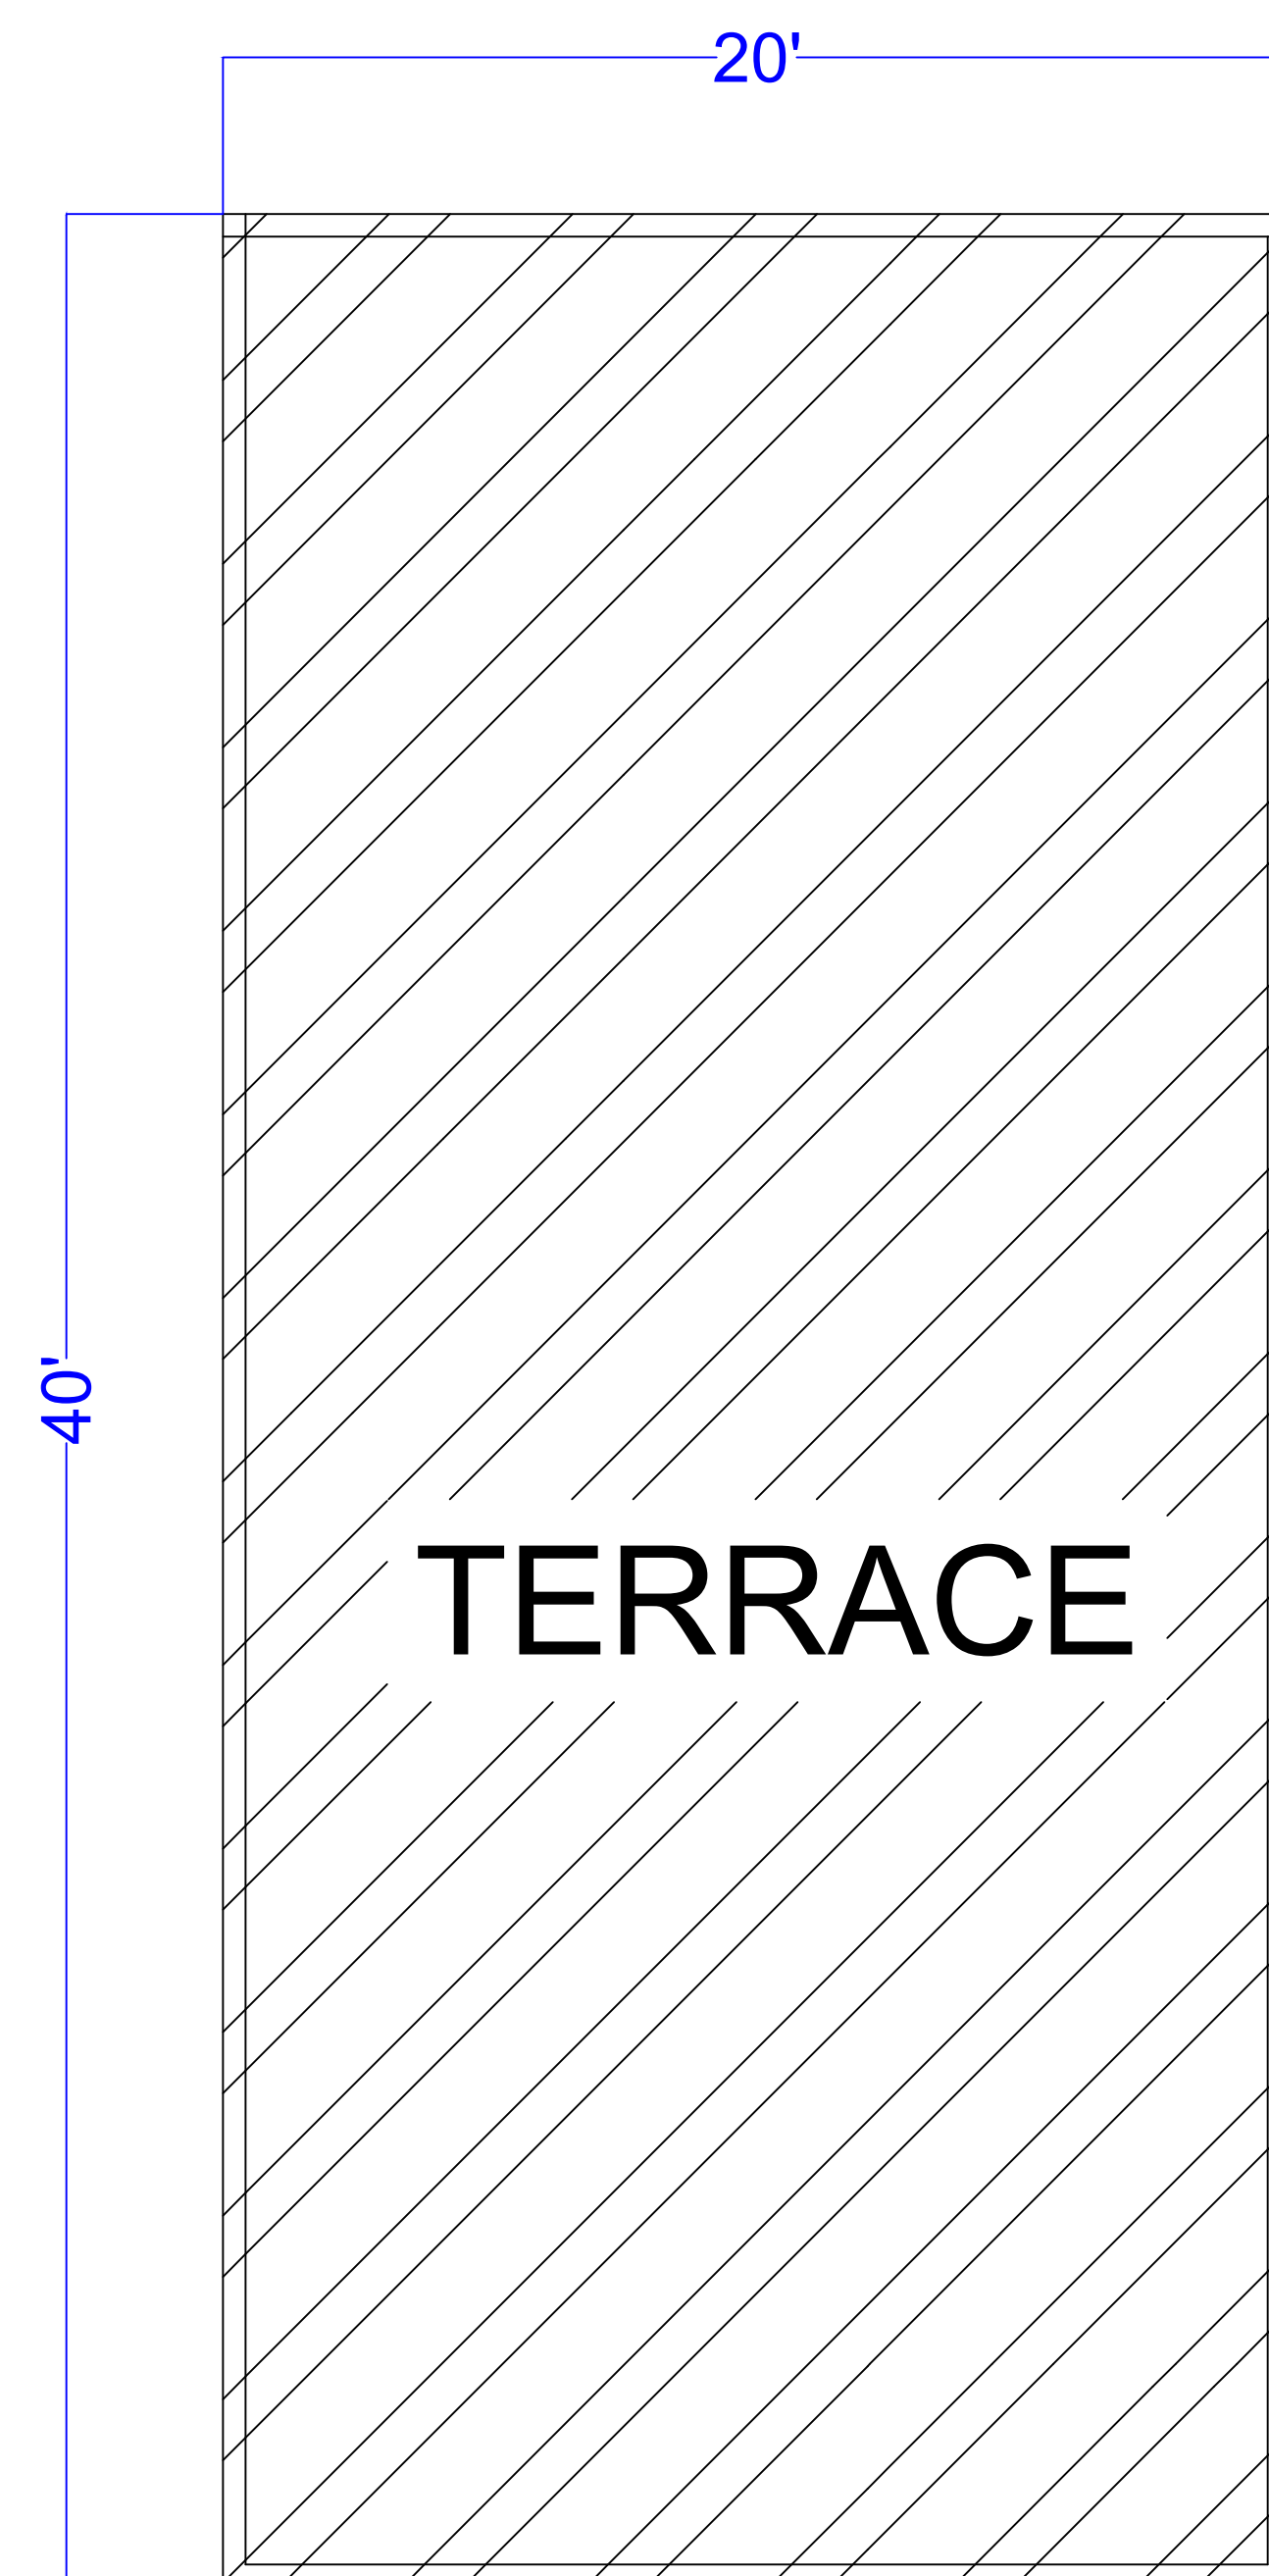

TERRACE PLAN

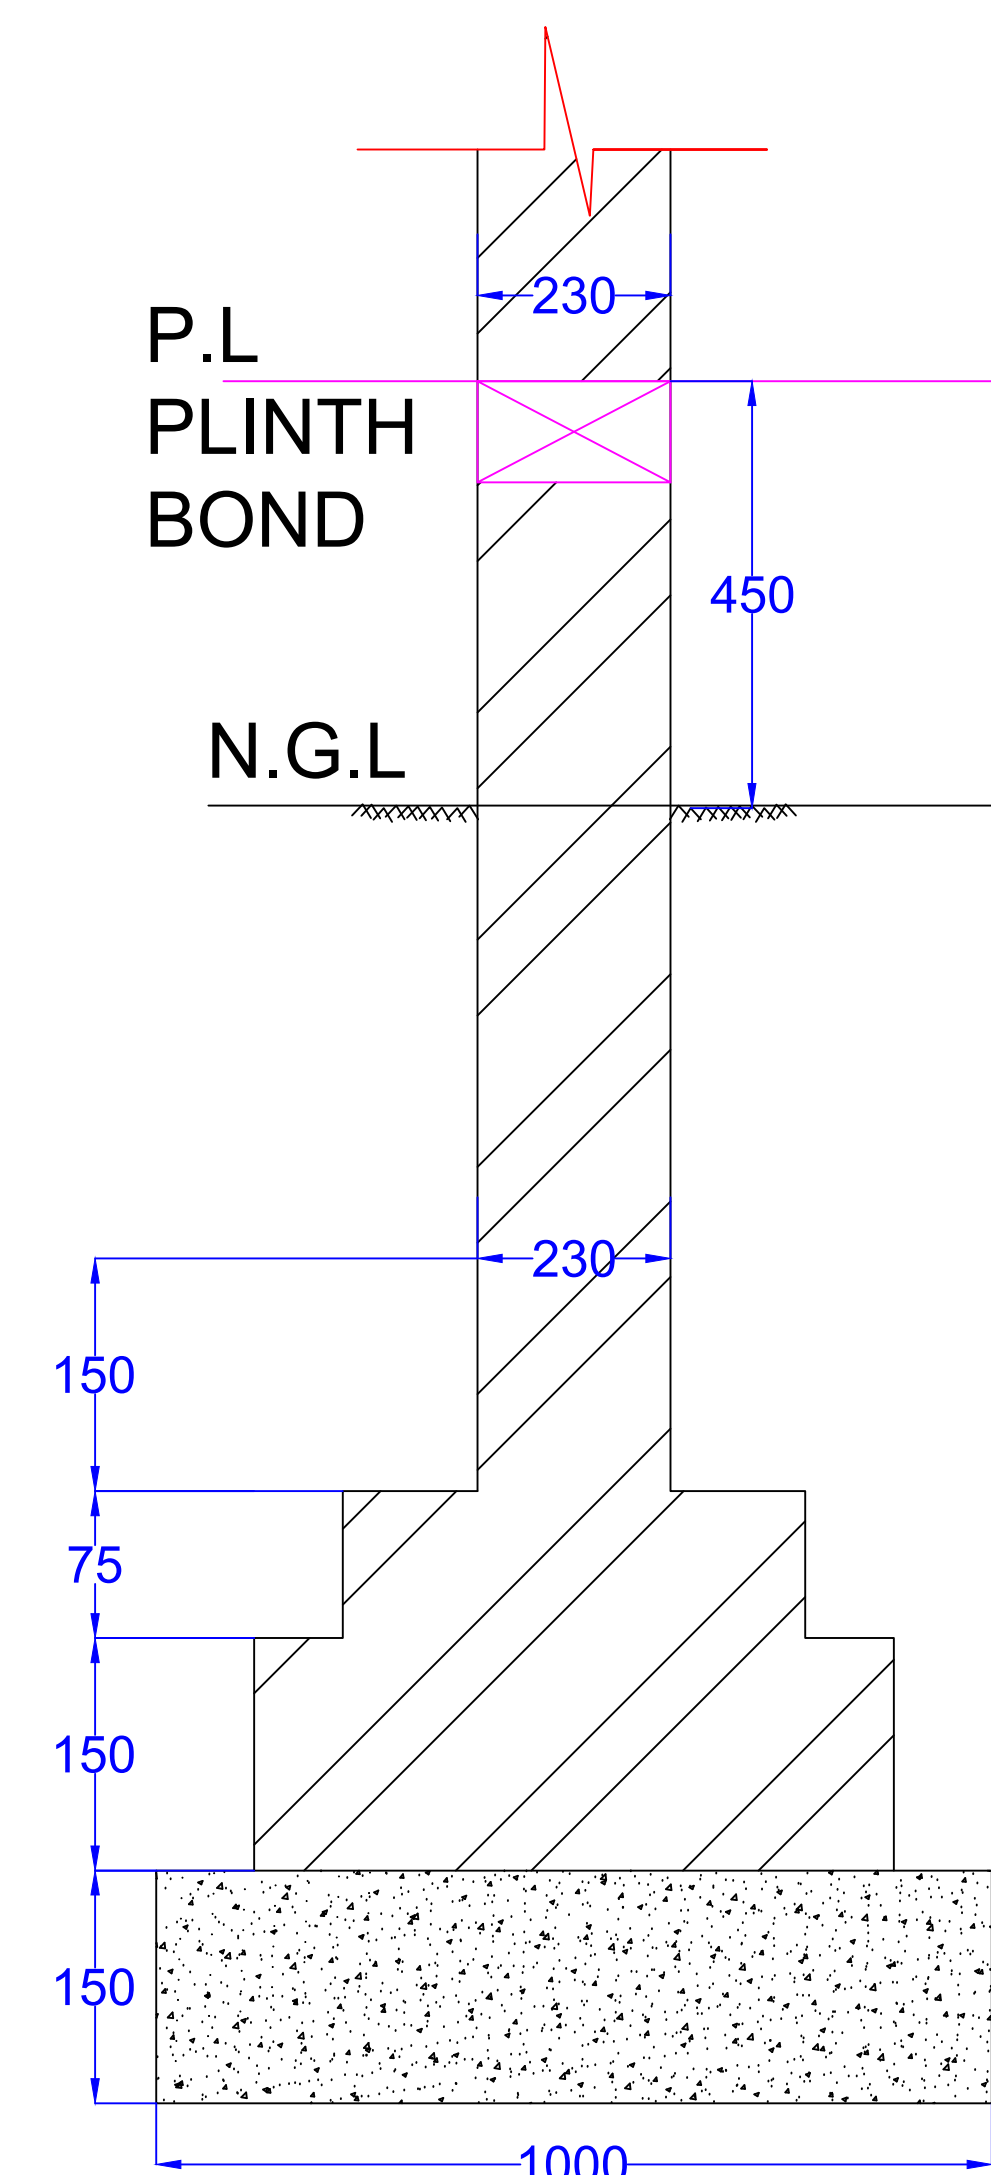

FOUNDATION
DETAIL
N.T.S

