
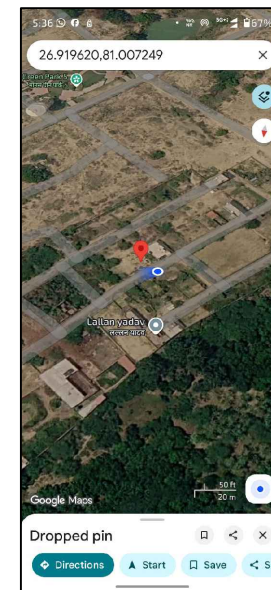
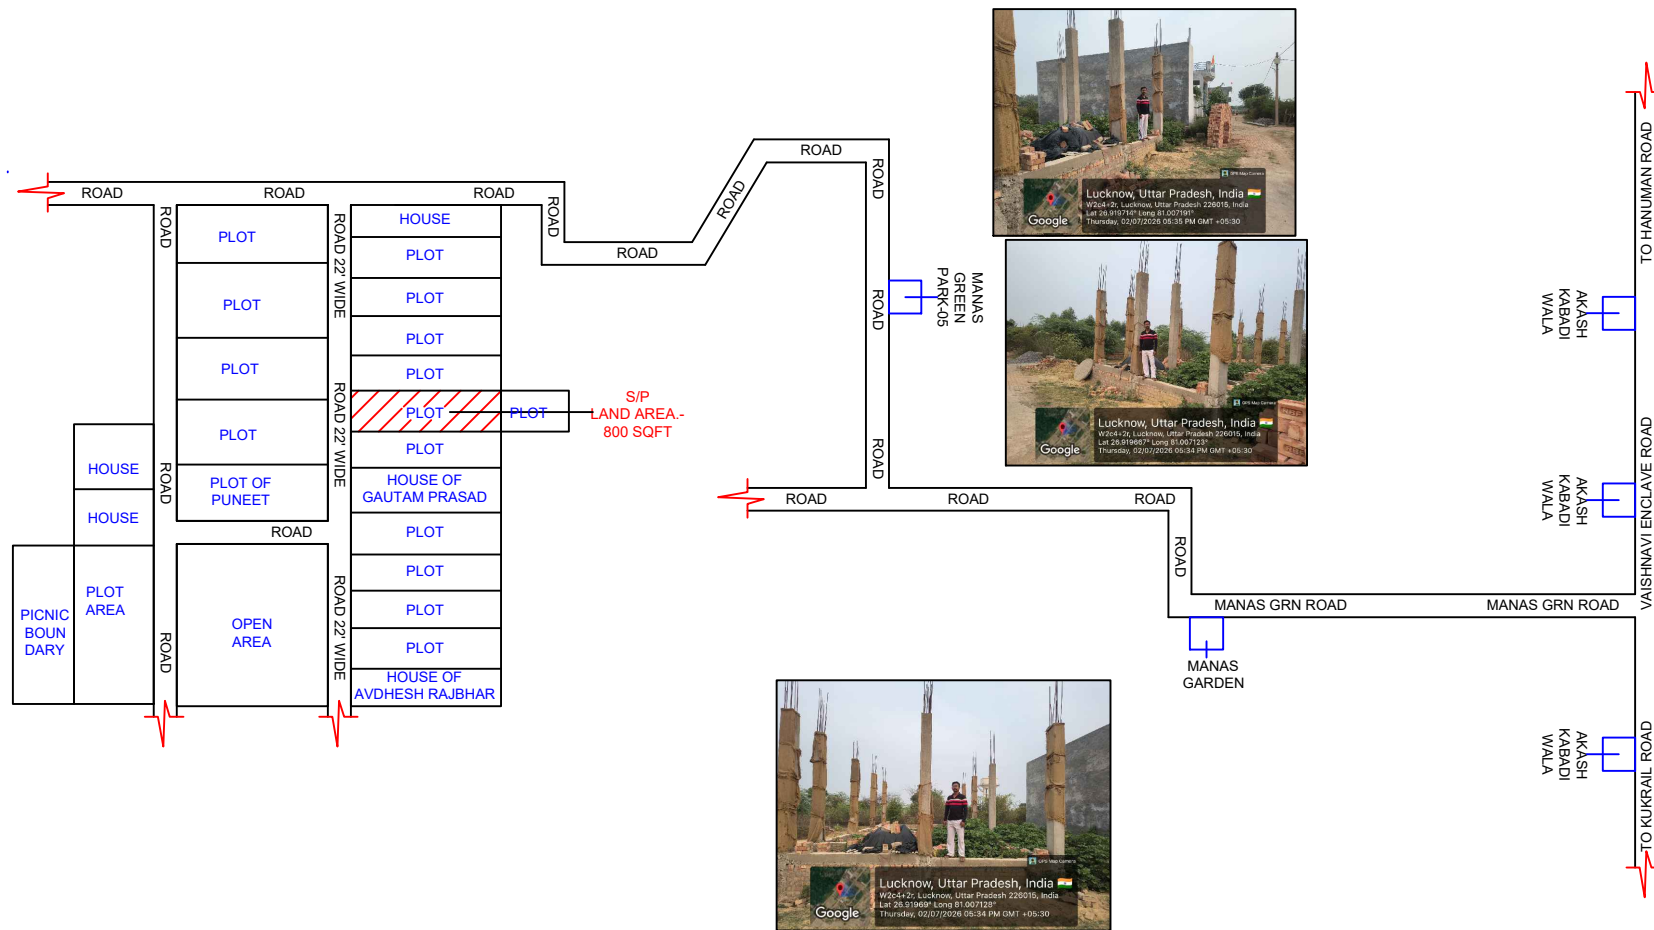


# LAYOUT//KEY ROUTE PLAN OF MRS.SHAKUNTALA SHUKLA W/O HARIKANT SHUKLA

WEST

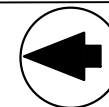

| CUSTOMER NAME<br>MRS.SHAKUNTALA SHUKLA W/O<br>HARIKANT SHUKLA                                                                     | BOUNDARY DETAIL<br>AS PER DOCUMENT   | BOUNDARY DETAIL<br>AS PER SITE                                                             | LATITUDE AND<br>LONGITUDE                    | PHOTOGRAPH | REMARKS   | ARCHITECT&ENGINEER<br>SING | CUSTOMERSING |
|---|---|--------------------------------------------------------------------------------------------|----------------------------------------------|------------|---|----------------------------|--------------|
| ADD.-PART OF PLOT NO-01,<br>PLOT PART OF KHASRA NO-82,<br>SITUATED AT VILL-JARHARA,<br>PARGANA,TEHSIL AND DISTRICT-<br>LUCKNOW,UP | EAST- PLOT DEEGAR<br>WEST- ROAD 22' WIDE<br>NORTH- THE REMAINING PORTION OF THE<br>PLOT FOR SALE IS SOLD BY SELLER<br>SOUTH- THE REMAINING PORTION OF THE<br>PLOT FOR SALE TO RUBY SRIVASTAVA | EAST- PLOT OF OTHER<br>WEST- ROAD 22' WIDE<br>NORTH- PLOT OF OTHER<br>SOUTH- PLOT OF OTHER | LATITUDE - 26.919620<br>LONGITUDE- 81.007249 |            | LAYOUT PLAN BASED<br>ONLY ON THE BASIS OF<br>PROPERTY SHOWN BY<br>THE CUSTOMER.<br>OWNERSHIP OF THE<br>PROPERTY CAN'T BE<br>VERIFIED BY US.<br>ALL DETAIL SARE<br>PROVIDED BY<br>CUSTOMER ONLY |                            |              |