
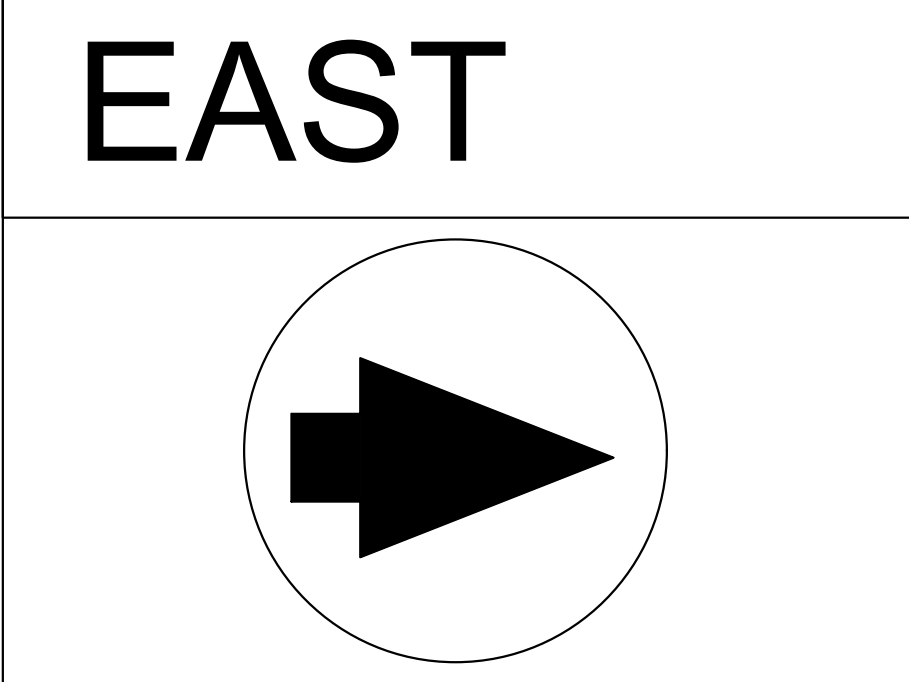
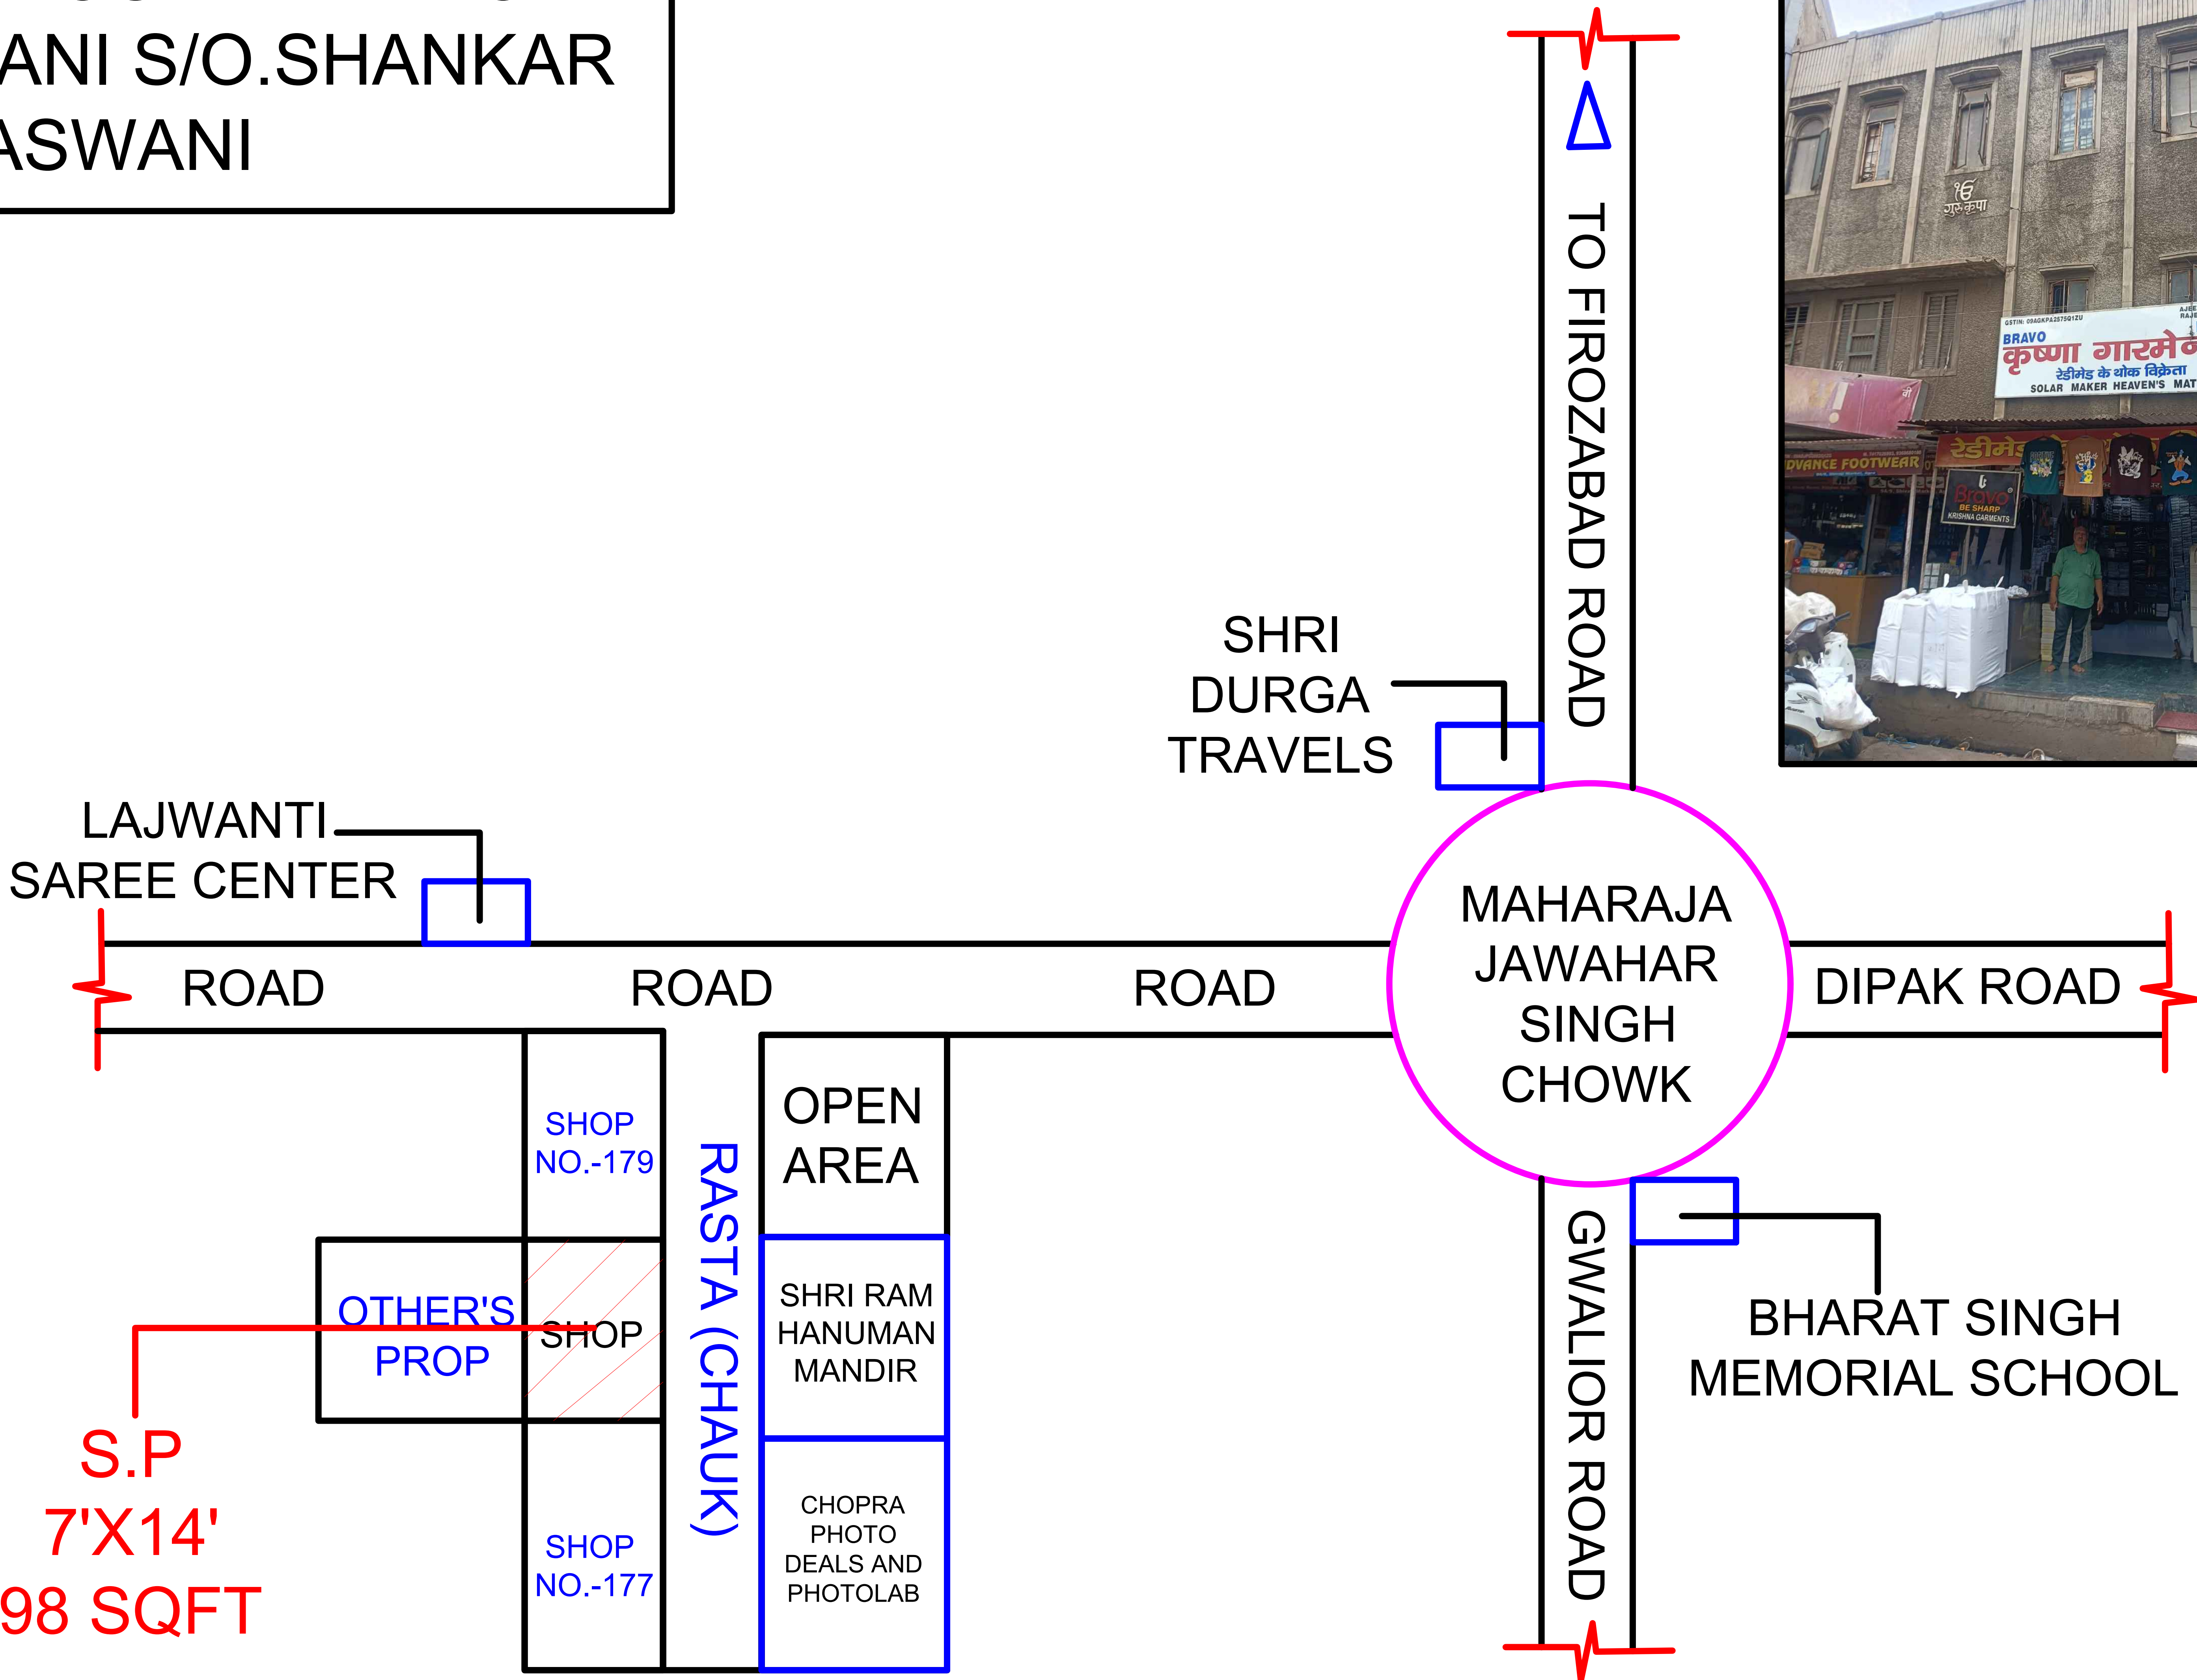


LAYOUT // KEY ROUTE PLAN OF
MR.AJEET AASWANI S/O.SHANKAR
LAL AASWANI

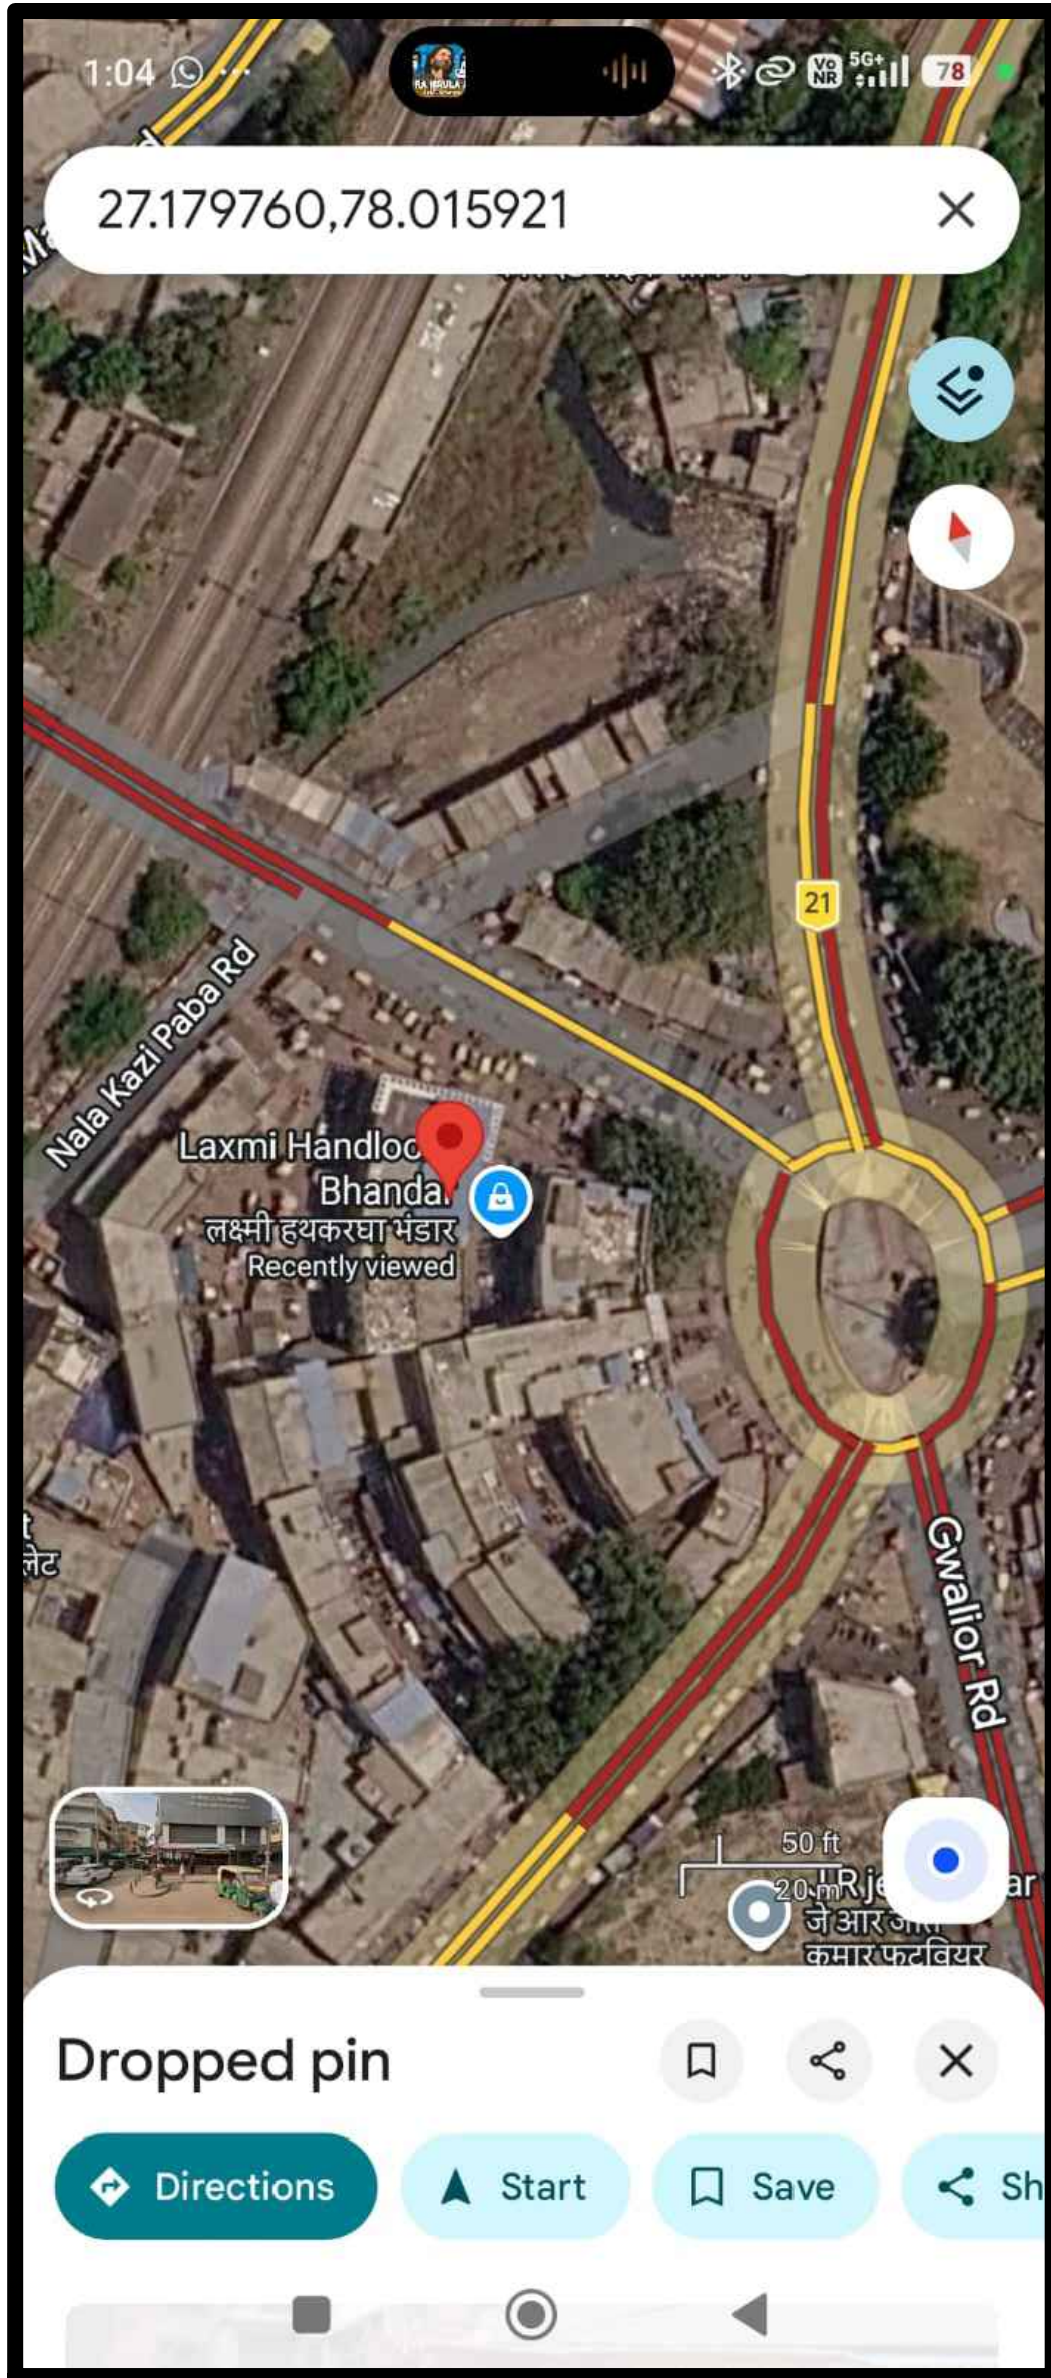

CUSTOMER NAME MR.AJEET AASWANI S/O.SHANKAR LAL AASWANI	BOUNDARY DETAIL AS PER DOCUMENT	BOUNDARY DETAIL AS PER SITE	LATITUDE AND LONGITUDE	PHOTOGRAPH	REMARKS	ARCHITECT&ENGINEER SING	CUSTOMERSING
ADD.-SHOP NO.-178,CORP NO.-9.A/8 AT-MITHAI KA CHABUTRA,SHIVAJI MARKET,WARD-NO.-07,TEHSIL AND DISTRICT-AGRA	EAST- RASTA (CHAUK) WEST.: OTHER'S PROP NORTH.: SHOP NO.-179 SOUTH.: SHOP NO.-177	EAST- RASTA (CHAUK) WEST.: OTHER'S PROP NORTH.: SHOP NO.-179 SOUTH.: SHOP NO.-177	LATITUDE-27.179760° LONGITUDE-78.015921°		LAYOUT PLAN BASED ONLY ON THE BASIS OF PROPERTY SHOWN BY THE CUSTOMER, OWNERSHIP OF THE PROPERTY CAN'T BE VERIFIED BY US. ALL DETAIL SARE PROVIDEDBY CUSTOMER ONLY		